





Recorded in Webster County, Missouri
Recording Date/Time: 03/27/2026 at 01:56:42 PM
Book: 1 Page: 1229

Pages: 1
Fee: \$44.00 8

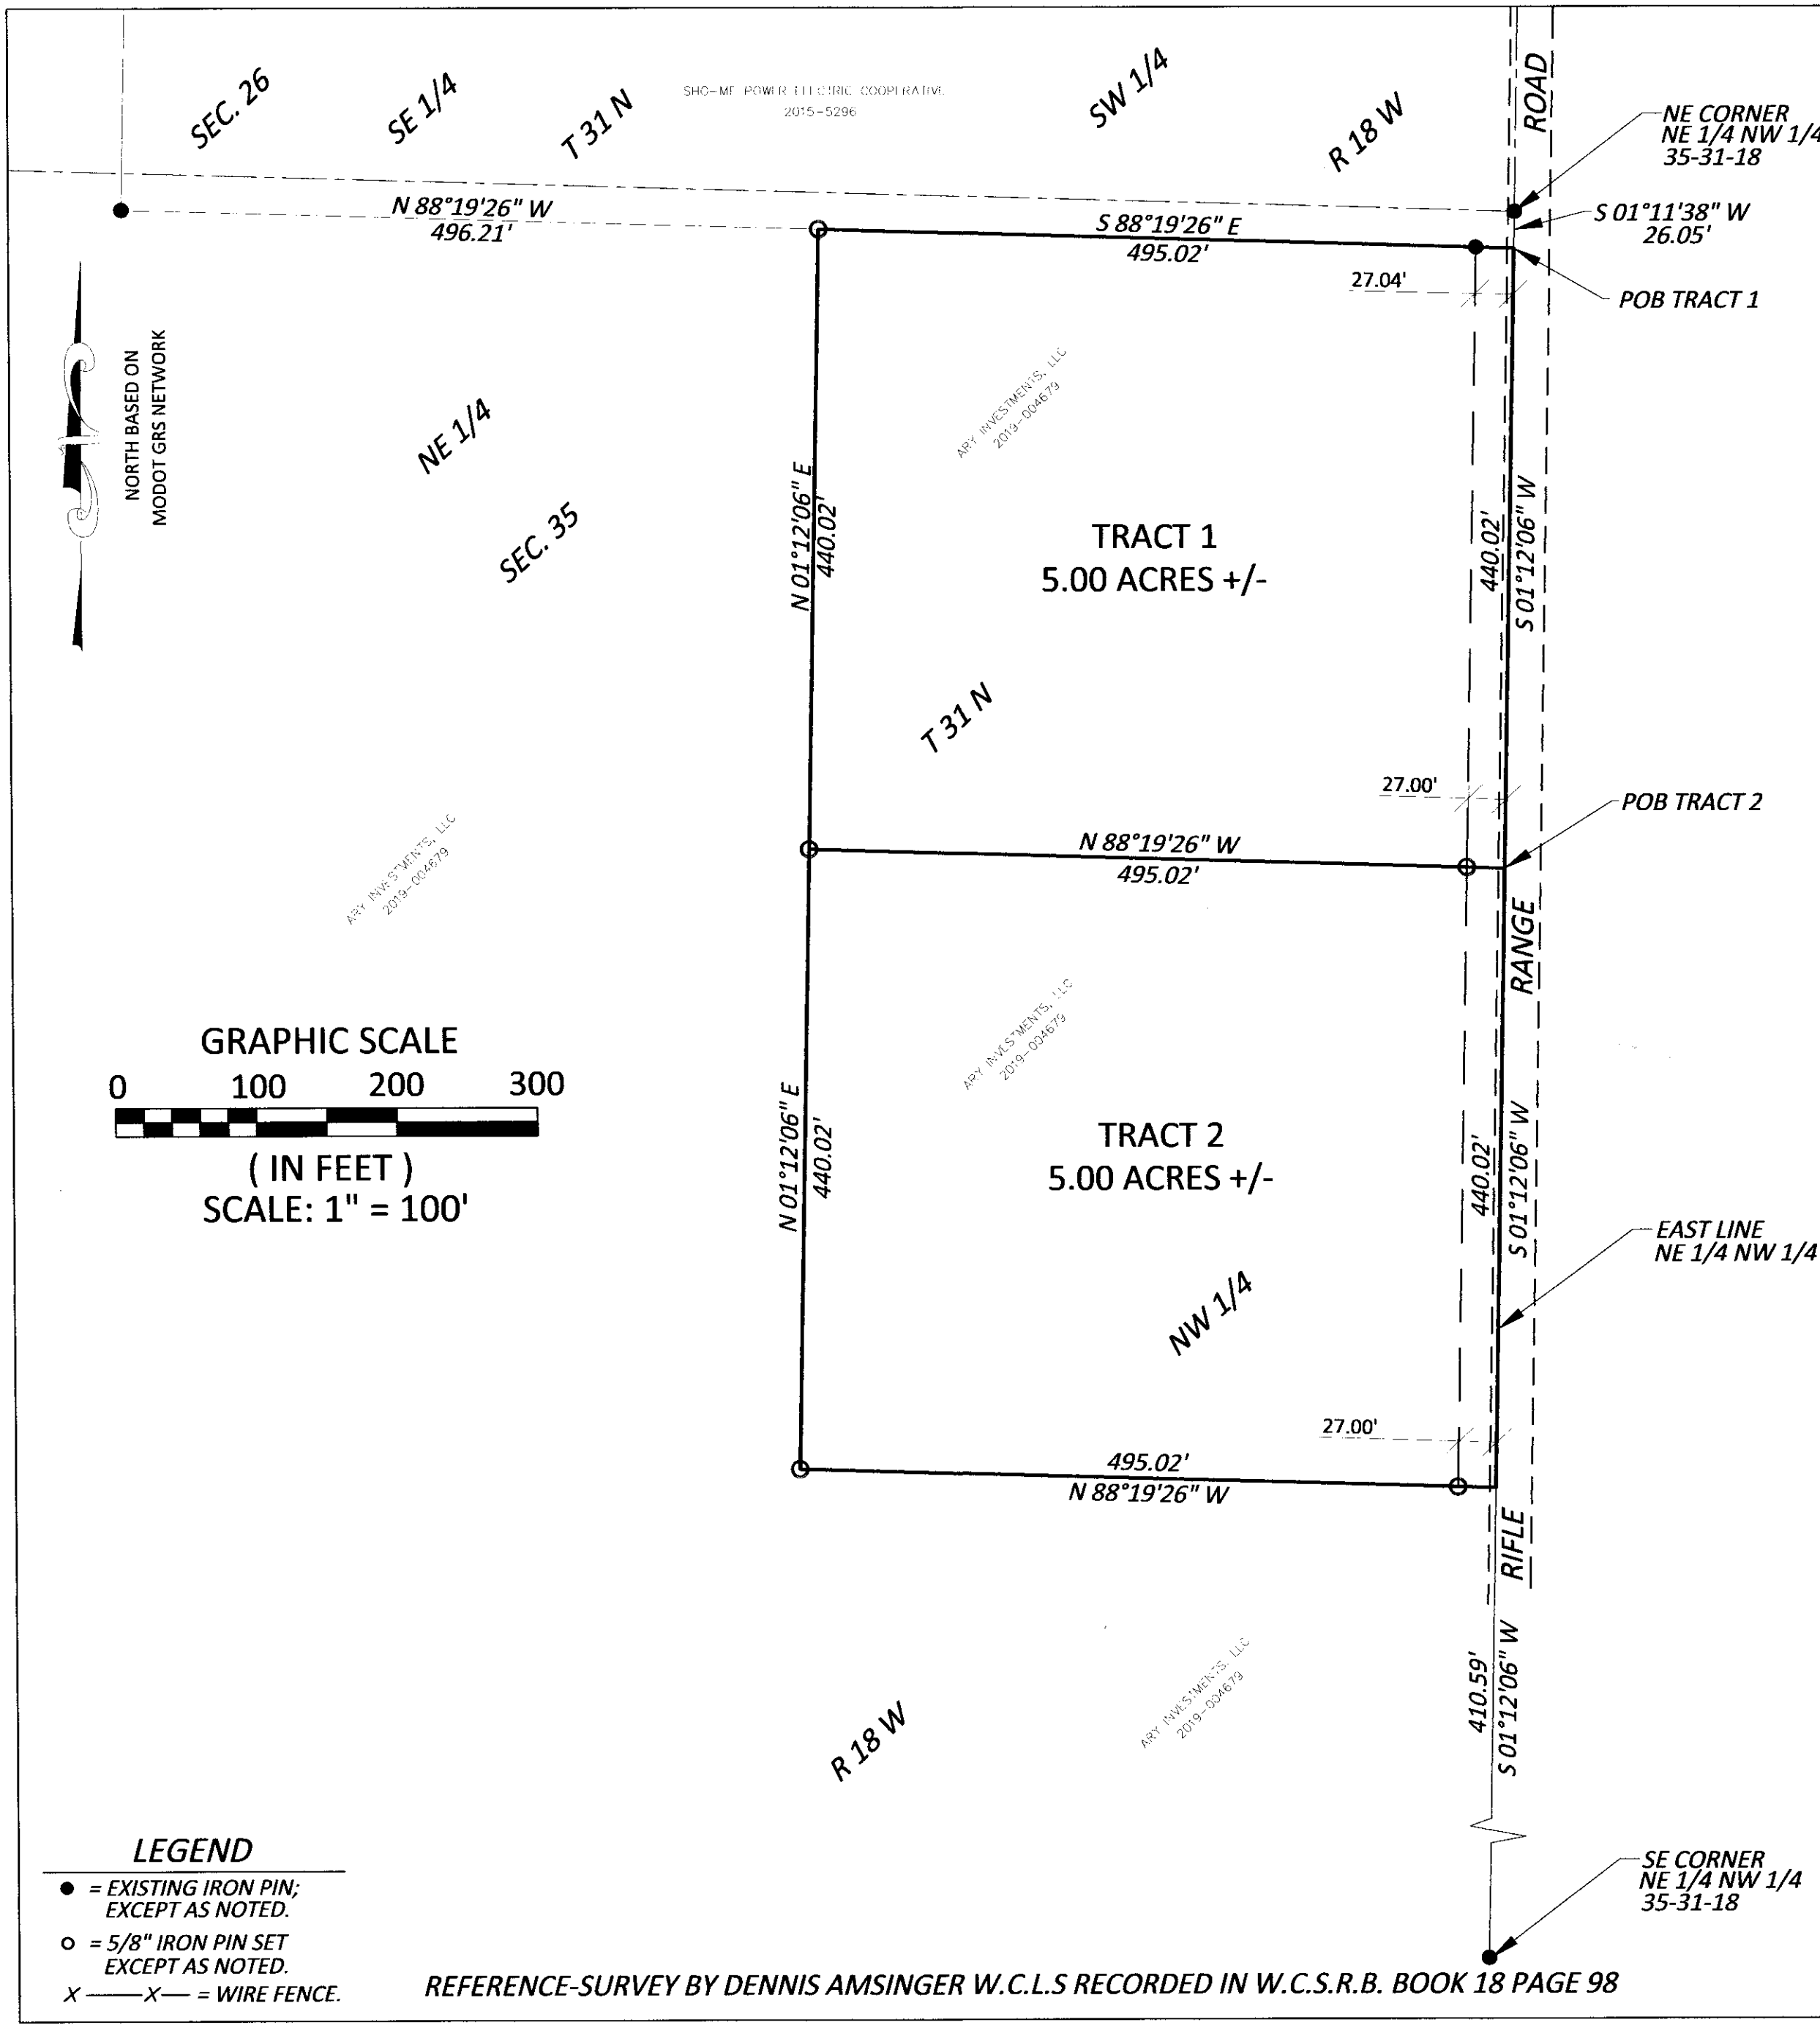

Stacy Attkisson
Recorder of Deeds

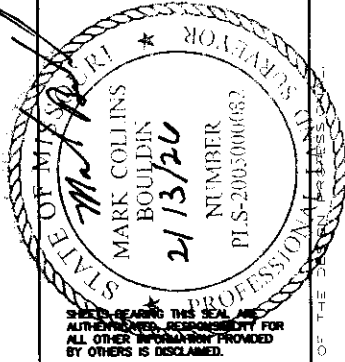

ADJOINING LAND OWNERS AND
THEIR DEED BOOK AND PAGE
NUMBERS MUST BE OBTAINED
FROM THE WEBSTER COUNTY
CLERK'S OFFICE OR FROM
WEBSTER COUNTY SURVEYOR
SERVICES (PROVIDED
BY OTHERS)

PROJECT:
ARY INVESTMENTS, LLC.
PO BOX C
MARSHFIELD, MO. 65706

BOUNDARY SURVEY

Buddy Webb & Company, Inc.
Land Surveyors
3051 EAST CALICO STREET
SPRINGFIELD, MISSOURI 65802
(417) 677-1305

REVISIONS:

PROJECT NO:
26-004

DATE:
FEBRUARY 12, 2026

SHEET NUMBER

1 OF 1

LEGAL DESCRIPTIONS

TRACT 1
A TRACT OF LAND BEING PART OF THE OF THE NORTHEAST QUARTER (NE 1/4) OF THE NORTHWEST QUARTER (NW 1/4) OF SECTION THIRTY FIVE (35), TOWNSHIP THIRTY ONE (31) NORTH, RANGE EIGHTEEN (18) WEST, AND BEING MORE PARTICULARLY DESCRIBED AS FOLLOWS: COMMENCING AT AN EXISTING IRON PIN AT THE NORTHEAST CORNER OF THE SAID NE 1/4 OF THE NW 1/4, THENCE S 1°11'38" W, AND ALONG THE EAST LINE OF THE SAID NE 1/4 OF THE NW 1/4, A DISTANCE OF 26.05 FEET, TO THE POINT OF BEGINNING; THENCE S 1°12'06" W, AND ALONG THE EAST LINE OF THE SAID NE 1/4 OF THE NW 1/4, A DISTANCE OF 440.02 FEET; THENCE N 88°19'26" W, A DISTANCE OF 495.02 FEET, TO AN IRON PIN SET; THENCE N 1°12'06" E, A DISTANCE OF 440.02 FEET, TO AN IRON PIN SET; THENCE S 88°19'26" E, A DISTANCE OF 495.02 FEET, TO THE POINT OF BEGINNING. SAID TRACT OF LAND CONTAINS 5.00 ACRES, MORE OR LESS, EXCEPT THAT PART TAKEN, DEEDED OR USED FOR ROAD PURPOSED ACROSS THE ENTIRE EAST SIDE THEREOF. SUBJECT TO ANY AND ALL EASEMENTS AND RESTRICTIONS OF RECORD. ALL IN WEBSTER COUNTY, MISSOURI.

TRACT 2
A TRACT OF LAND BEING PART OF THE OF THE NORTHEAST QUARTER (NE 1/4) OF THE NORTHWEST QUARTER (NW 1/4) OF SECTION THIRTY FIVE (35), TOWNSHIP THIRTY ONE (31) NORTH, RANGE EIGHTEEN (18) WEST, AND BEING MORE PARTICULARLY DESCRIBED AS FOLLOWS: COMMENCING AT AN EXISTING IRON PIN AT THE NORTHEAST CORNER OF THE SAID NE 1/4 OF THE NW 1/4, THENCE S 1°11'38" W, AND ALONG THE EAST LINE OF THE SAID NE 1/4 OF THE NW 1/4, A DISTANCE OF 26.05 FEET; THENCE S 1°12'06" W, AND ALONG THE EAST LINE OF THE SAID NE 1/4 OF THE NW 1/4, A DISTANCE OF 440.02 FEET, TO THE POINT OF BEGINNING; THENCE S 1°12'06" W, AND ALONG THE EAST LINE OF THE SAID NE 1/4 OF THE NW 1/4, A DISTANCE OF 440.02 FEET; THENCE N 88°19'26" W, A DISTANCE OF 495.02 FEET, TO AN IRON PIN SET; THENCE N 1°12'06" E, A DISTANCE OF 440.02 FEET, TO AN IRON PIN SET; THENCE S 88°19'26" E, A DISTANCE OF 495.02 FEET, TO THE POINT OF BEGINNING. SAID TRACT OF LAND CONTAINS 5.00 ACRES, MORE OR LESS, EXCEPT THAT PART TAKEN, DEEDED OR USED FOR ROAD PURPOSED ACROSS THE ENTIRE EAST SIDE THEREOF. SUBJECT TO ANY AND ALL EASEMENTS AND RESTRICTIONS OF RECORD. ALL IN WEBSTER COUNTY, MISSOURI.

DECLARATION BY SURVEYOR

I HEREBY DECLARE TO: ARY INVESTMENTS, LLC.
THAT THE INFORMATION CONTAINED HEREIN IS BASED UPON AN ACTUAL SURVEY OF THE LAND DESCRIBED HEREIN, WHICH WAS PERFORMED TO THE BEST OF MY KNOWLEDGE AND BELIEF, IN ACCORDANCE WITH THE JOINT STANDARDS FOR PROPERTY SURVEYS AS PUBLISHED BY THE MISSOURI DEPARTMENT OF NATURAL RESOURCES AND THE MISSOURI BOARD FOR ARCHITECTS, PROFESSIONAL ENGINEERS AND PROFESSIONAL LAND SURVEYORS, JUNE 30, 2017, AND BASED ON INFORMATION PROVIDED BY; ARY INVESTMENTS, LLC.

MONUMENTS AND PINS SHOWN AS SET WERE PLACED UNDER MY PERSONAL SUPERVISION

PHYSICAL EVIDENCE OF IMPROVEMENTS ARE SHOWN FROM INFORMATION TAKEN BY VISUAL INSPECTION OF THE PREMISES. EASEMENTS SHOWN ARE THOSE WRITTEN, PROVIDED, OR DISCOVERED AND MAY NOT BE ALL INCLUSIVE.

APPARENT OWNERSHIPS AS SHOWN ARE BASED UPON INFORMATION PROVIDED BY OTHERS AND DO NOT REPRESENT AN OPINION AS TO TITLE.

THIS PLAT OF SURVEY IS AN INSTRUMENT OF SERVICE AND IS NOT TO BE USED BY ANYONE OTHER THAN THOSE TO WHOM IT HAS BEEN CERTIFIED UNLESS IT HAS BEEN UPDATED AND RE-CERTIFIED BY THE UNDERSIGNED.

Mark C. Bouldin
MARK C. BOULDIN
MISSOURI P.L.S. 2005000082
BUDDY WEBB & COMPANY, INC.
LICENSE #2021019889

CLASS OF PROPERTY = RURAL PROPERTY